



Escena 01 — Vista principal de referencia

Reproducción de la cámara de la escena 01 del archivo .skp (generada desde la geometría del modelo).

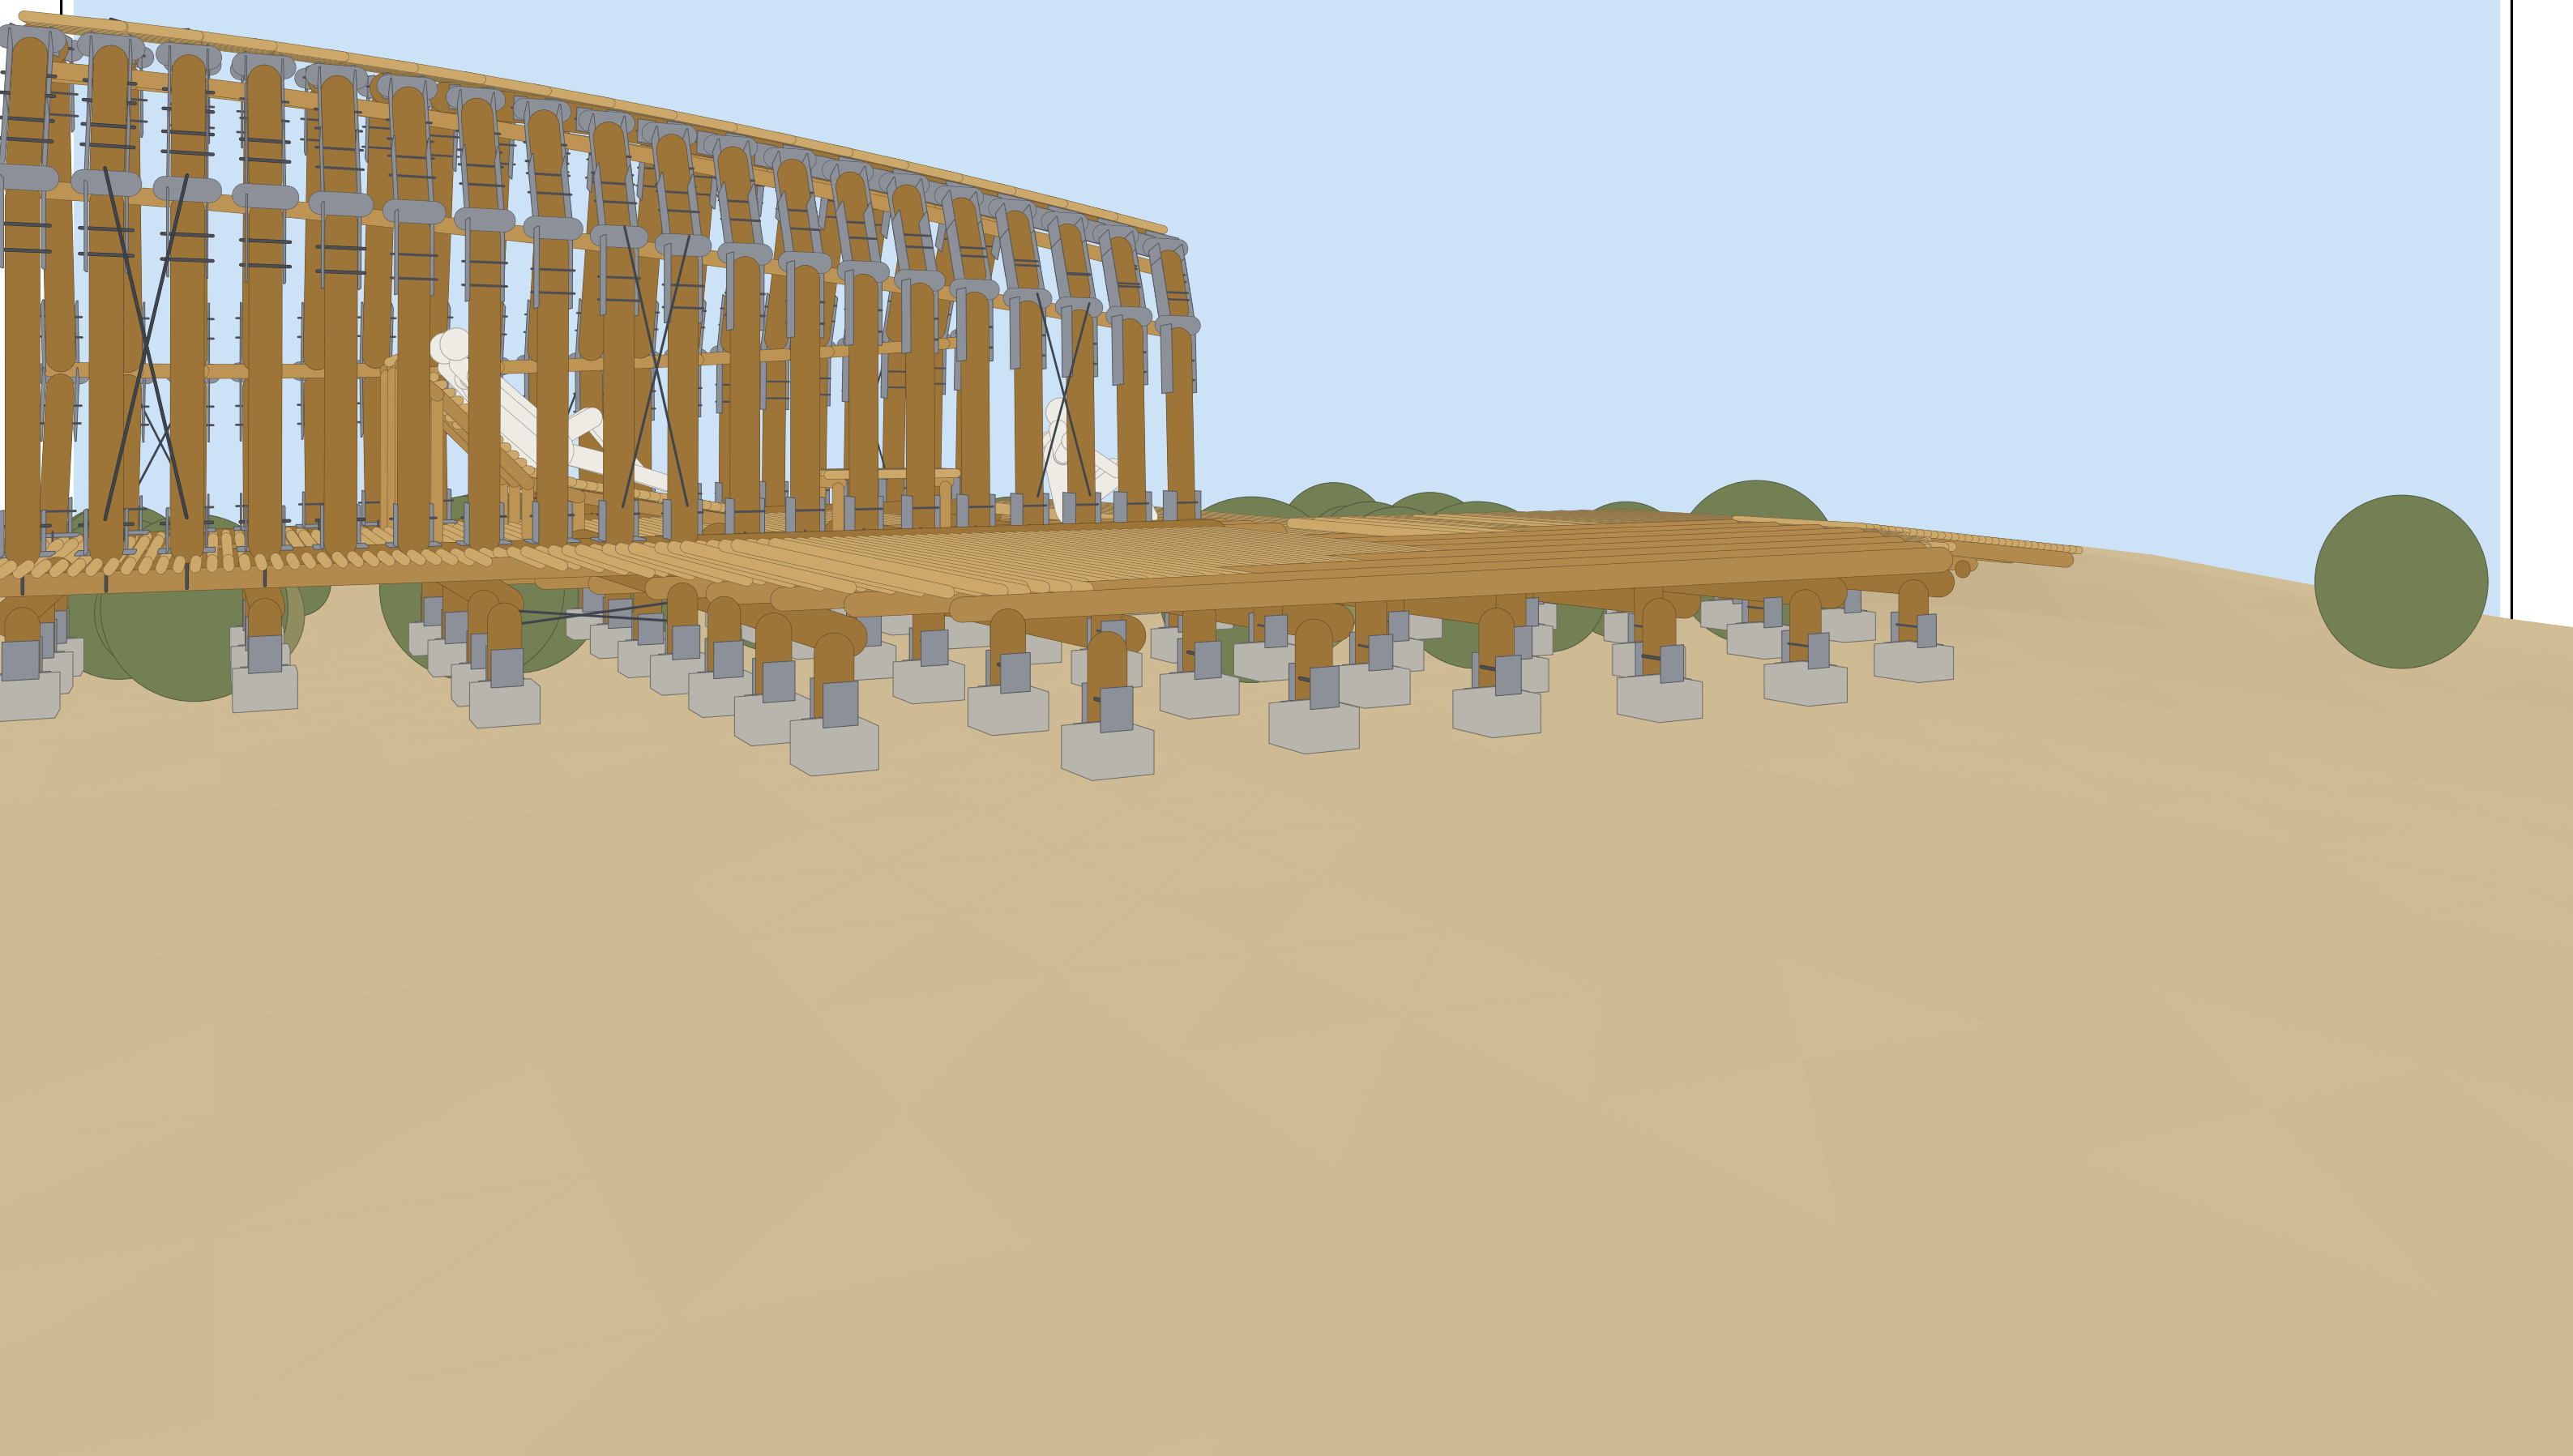

Planta general (se omite la cubierta permeable de latillas para leer pórticos y mobiliario)

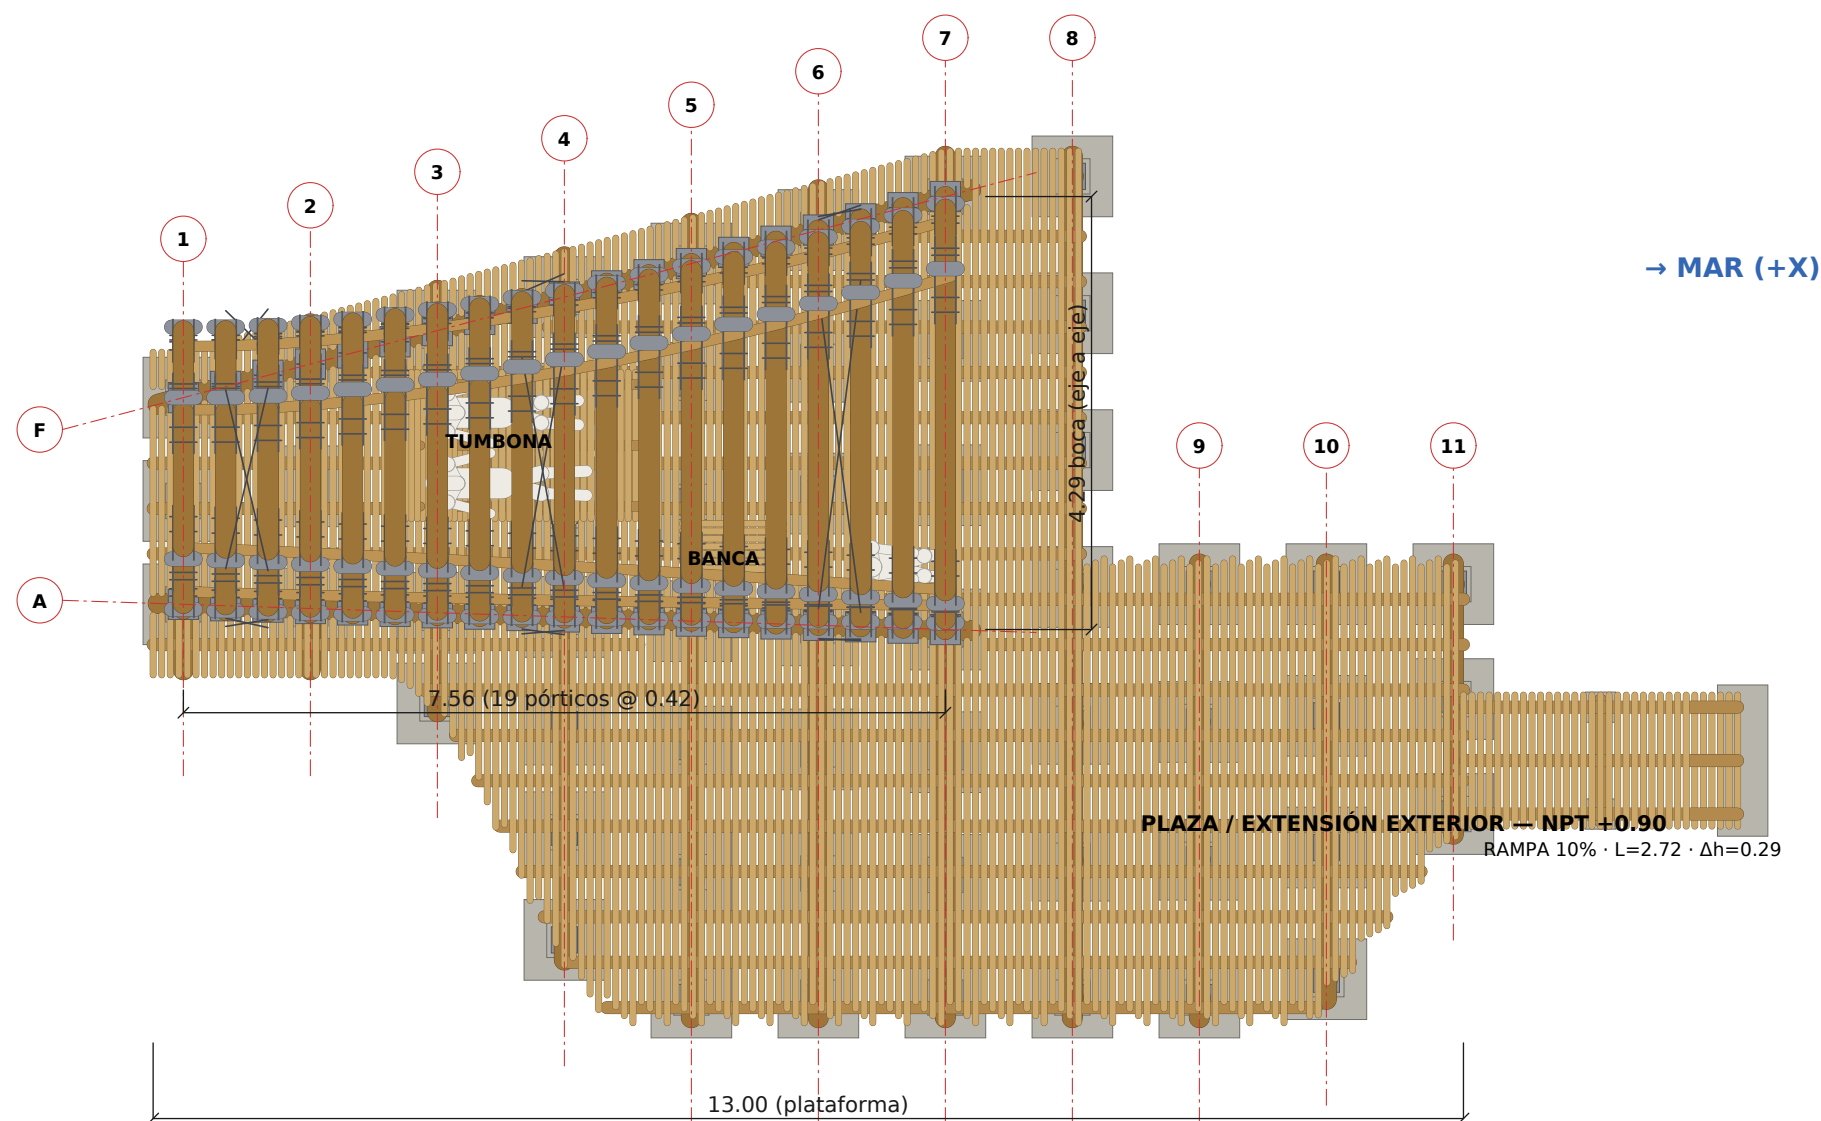

L-02


REFUGIO COSTERO DE CAÑA — PROPUESTA CONSTRUCTIVA V01

Planta general: huella de plataforma, pórticos, asientos, apoyos y cotas


Escala: 1:75 (A3) · Unidades: metros · NPT +0.90 (datum ±0.00)

Nivel 2: propuesta preliminar. NO apta para construcción sin cálculo estructural, estudio de suelos (E.050) y revisión de profesional colegiado.

Elevación lateral (corte de terreno en y = -0.30)

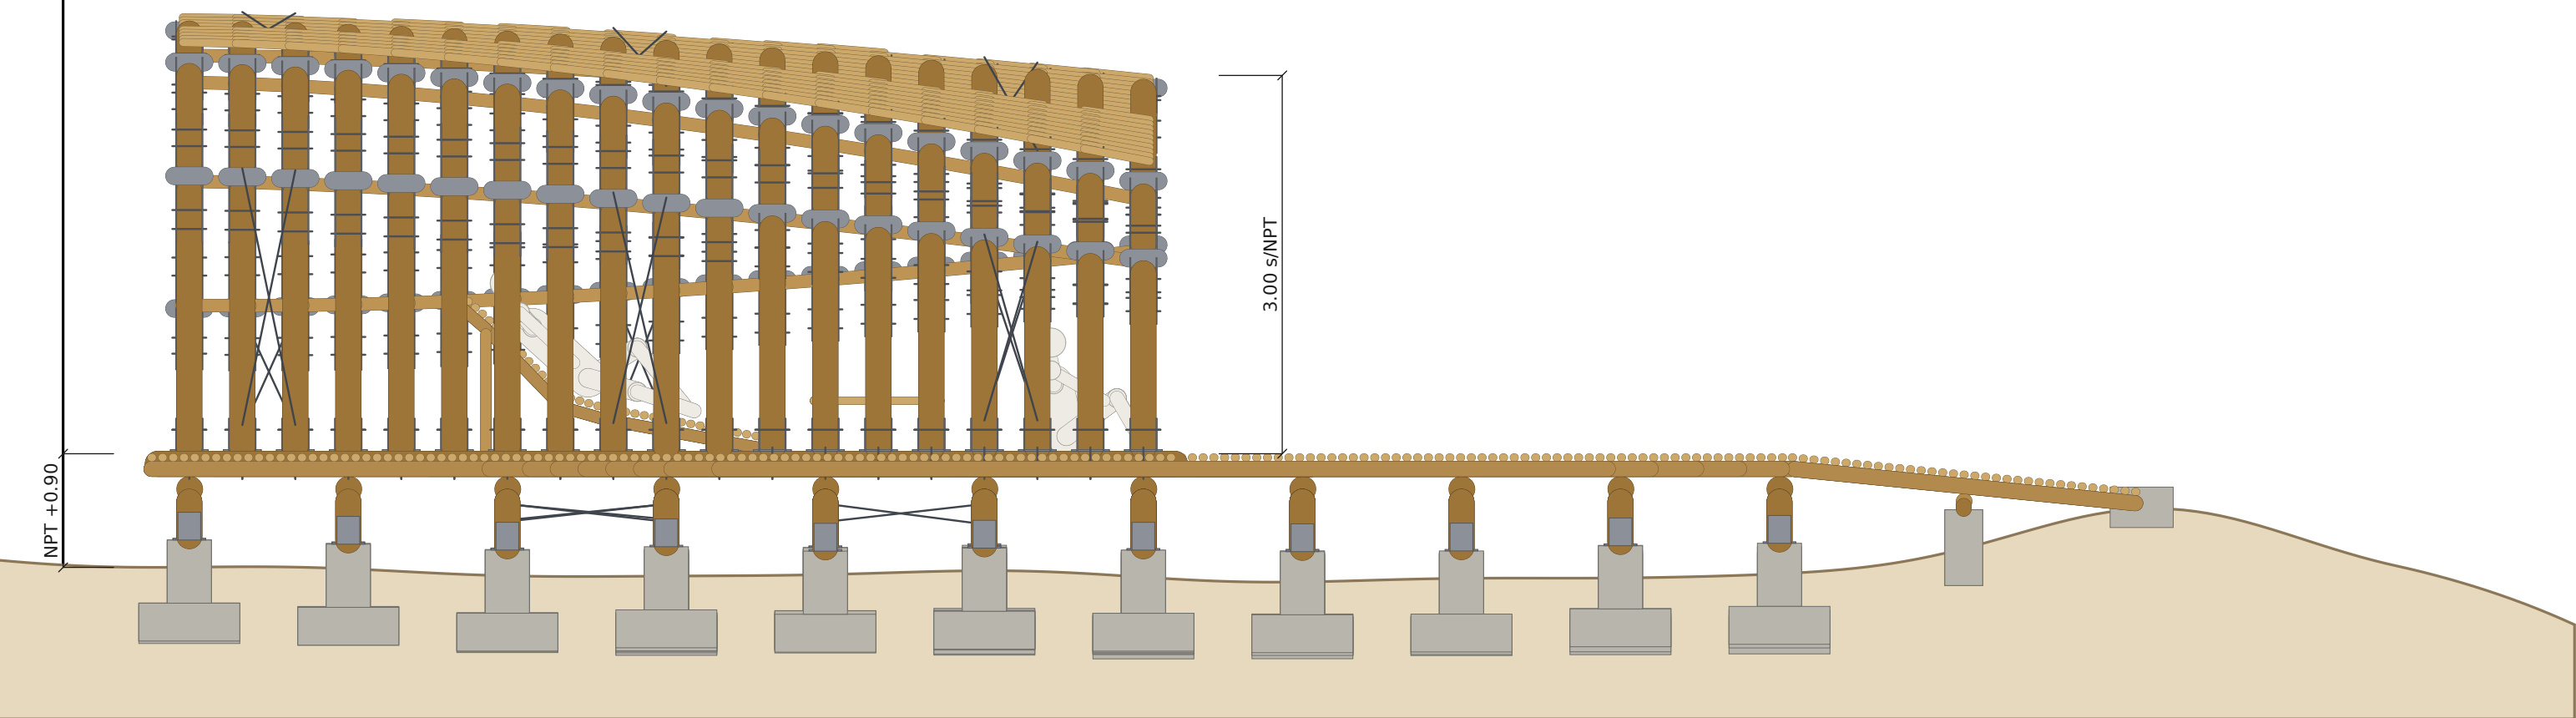

Elevación posterior (desde -X)

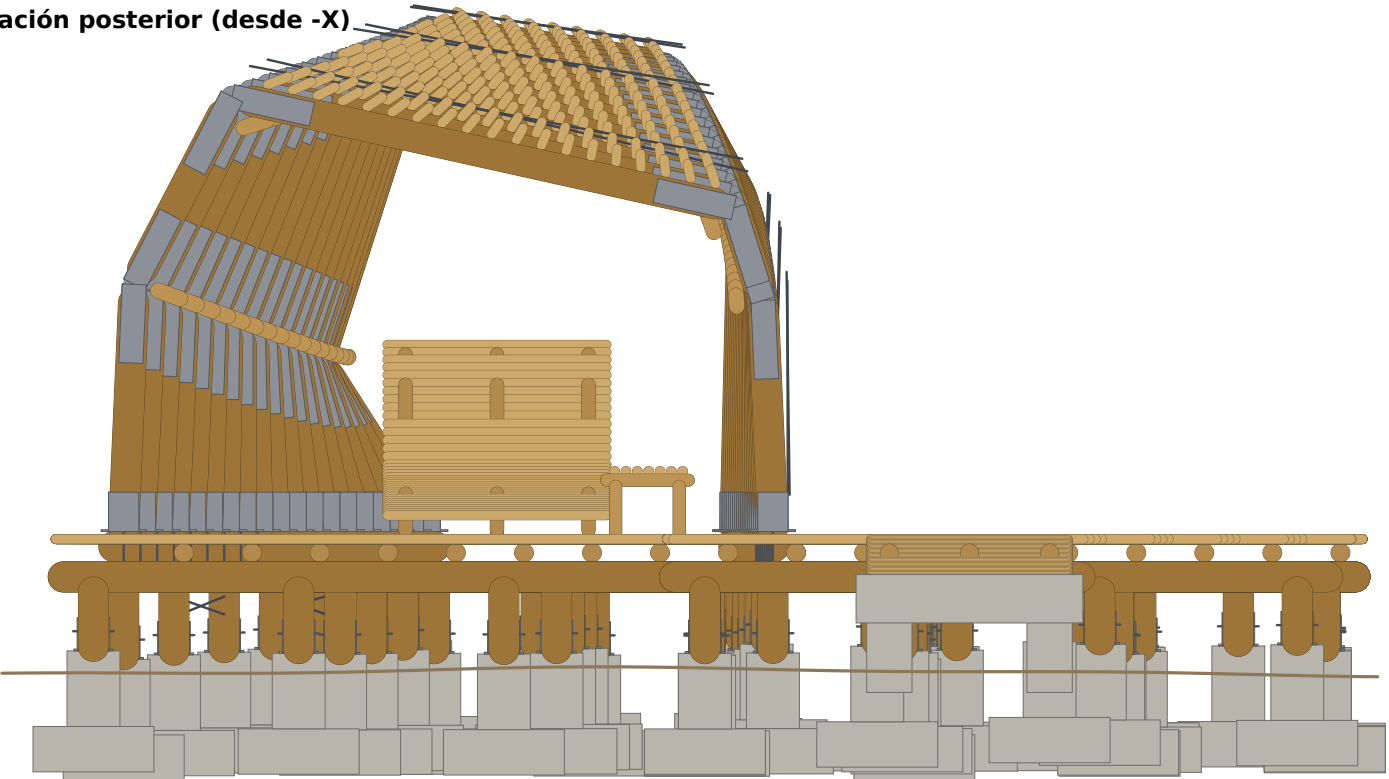

L-03

REFUGIO COSTERO DE CAÑA — PROPUESTA CONSTRUCTIVA V01

Elevación lateral (desde el lado cercano, -Y) y elevación posterior (desde -X)


Escala: 1:50 (A3) · Unidades: metros · NPT +0.90 (datum ±0.00)

Nivel 2: propuesta preliminar. NO apta para construcción sin cálculo estructural, estudio de suelos (E.050) y revisión de profesional colegiado.

Pórtico de la boca — longitudes de eje (m)

A-B	1.500
B-C	0.641
C-D	3.400
D-E	1.400
E-F	1.606
A-F (luz)	4.294

Rumbos de eje: 87.5°, 72.5°, 12.5°, -62.5°, -87.5°
Vista desde el mar (+X): el lado cercano (A) queda a la DERECHA.

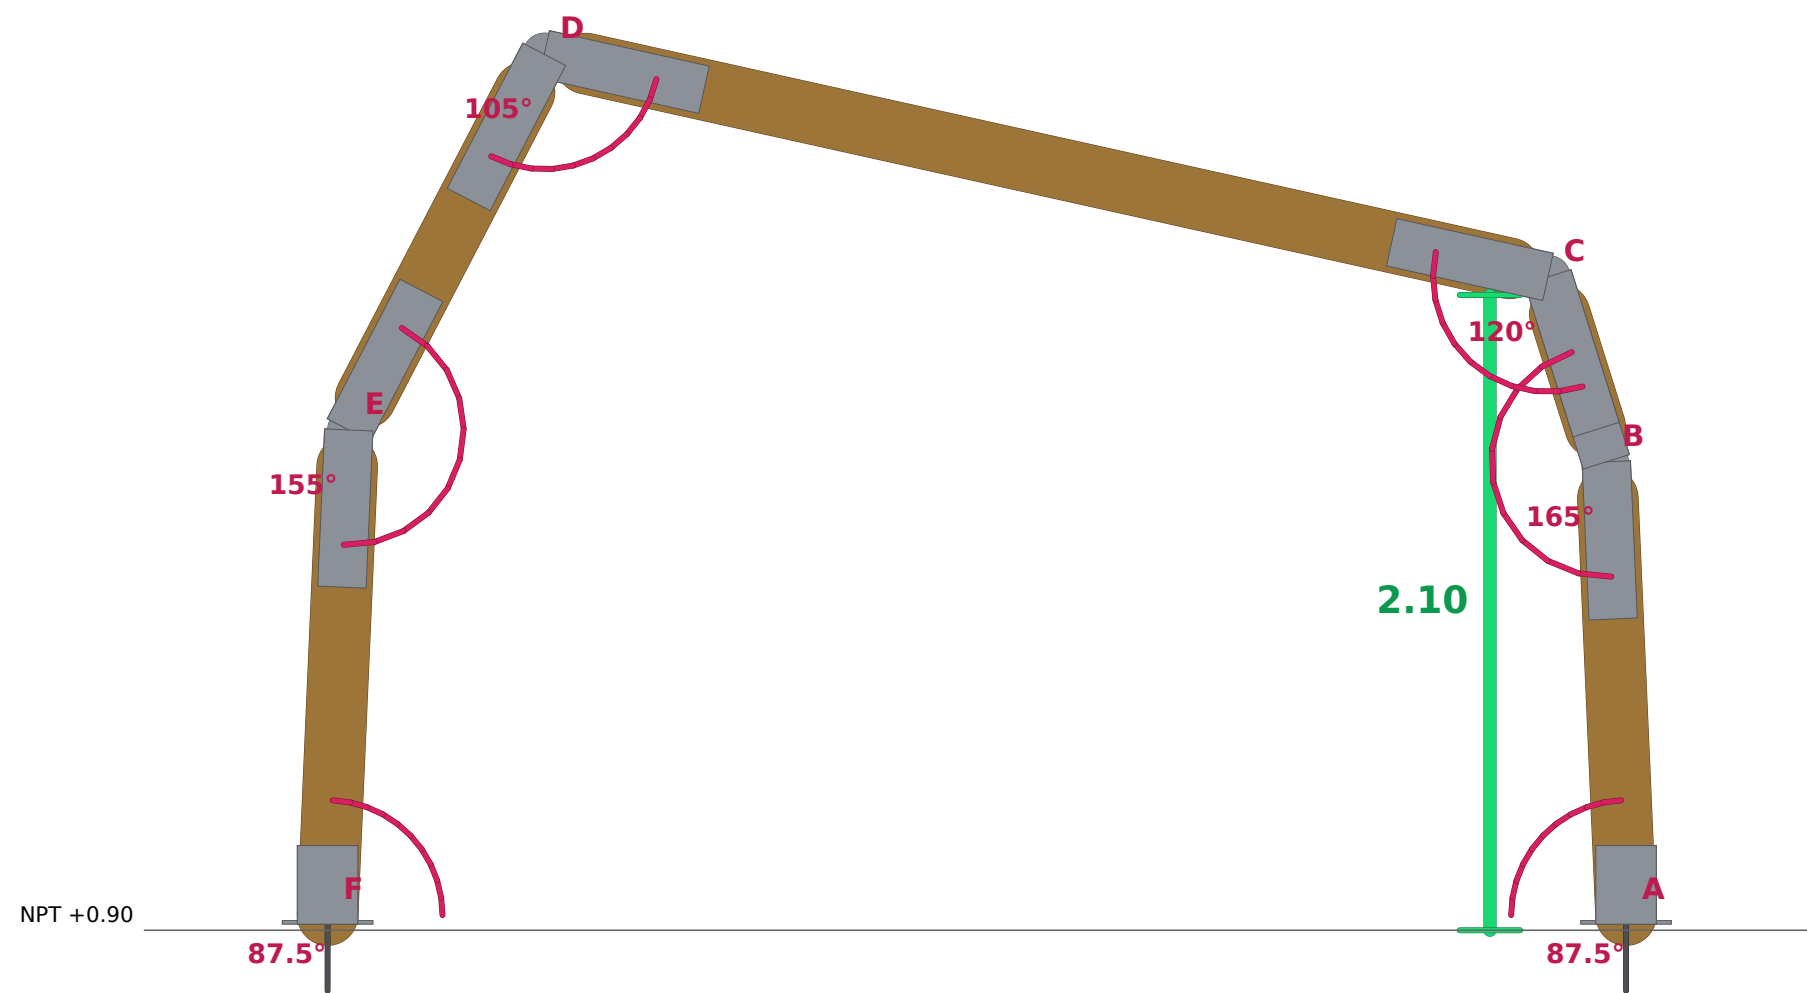

Ángulos interiores del hexágono de la boca: B=165°, C=120°, D=105°, E=155° (referencia 4).
Pies A y F = 87.5° c/u: cierre geométrico (105+120+155+165 = 545°; 720-545 = 175°).
Cota verde: NPT (+0.90) a cara inferior de la viga C-D, a 0.45 m del pie cercano = 2.10 m.

L-04


REFUGIO COSTERO DE CAÑA — PROPUESTA CONSTRUCTIVA V01

Elevación frontal / sección por la boca (pórtico 19): ángulos de referencia y cota de 2.10 m


Escala: 1:25 (A3) · Unidades: metros · NPT +0.90 (datum ±0.00)

Nivel 2: propuesta preliminar. NO apta para construcción sin cálculo estructural, estudio de suelos (E.050) y revisión de profesional colegiado.

Planta de cimentación: 56 apoyos (zapatas aisladas + pedestales)

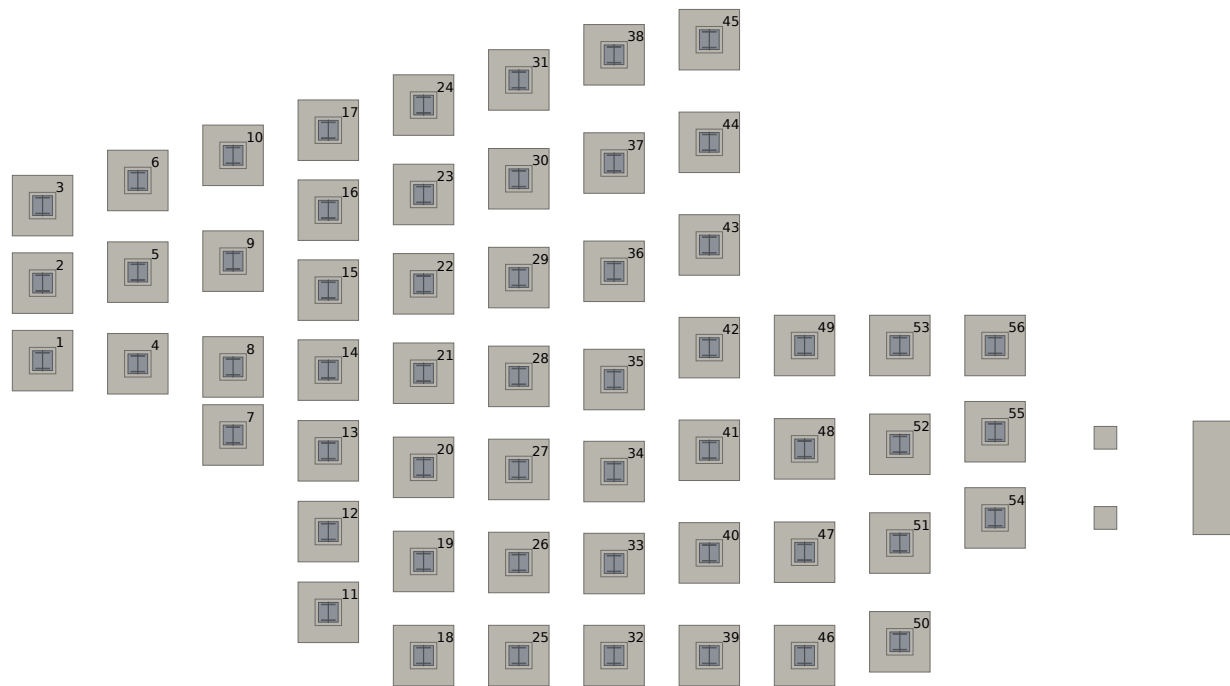


DETALLE 1 — APOYO TIPO (esquemático, sin escala exacta)

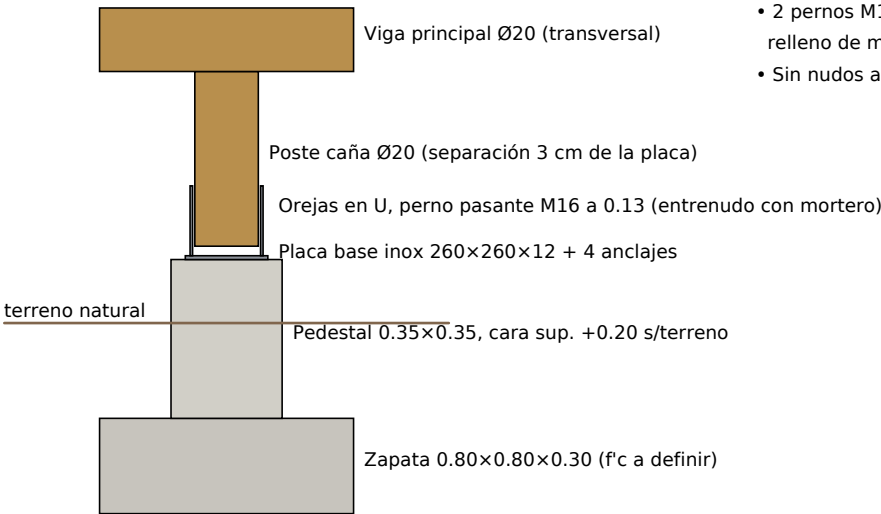

DETALLE 2 — NODO DE PÓRTICO (B, C, D, E)

- Corte de cada caña a $\geq (r+12 \text{ mm})/\text{sen}(\theta/2)$ del vértice para no interferir.
- Pletinas inox 8 mm a ambas caras + pasador central Ø14 (rigidez de nudo).
- 2 pernos M16 por extremo; 1.º perno a $\geq 150 \text{ mm}$ del corte, en entrenado relleno de mortero (práctica E.100 / ISO 22156, a verificar por cálculo).
- Sin nudos articulados puros: el pórtico necesita nudo resistente a momento.

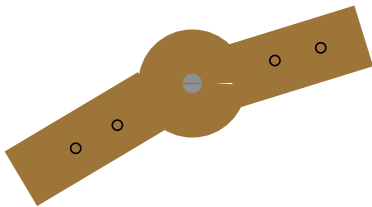

Hipótesis sin validar: suelo arenoso compacto, capacidad admisible a definir por EMS (E.050).
Zapata 0.80x0.80x0.30, fondo -0.60 bajo terreno; pedestal 0.35x0.35 hasta +0.20 sobre terreno.
Ninguna caña en contacto con el suelo. Anclaje en U inox AISI 316 + perno M16, entrenado relleno de mortero. Separación mínima entre apoyos: 0.90 m.

L-05

REFUGIO COSTERO DE CAÑA — PROPUESTA CONSTRUCTIVA V01

Planta de cimentación y detalles preliminares de unión — PENDIENTE DE CÁLCULO

Escala: planta 1:100 · detalles 1:10 · Unidades: metros · NPT +0.90 (datum ±0.00)

Nivel 2: propuesta preliminar. NO apta para construcción sin cálculo estructural, estudio de suelos (E.050) y revisión de profesional colegiado.