


Escena 01 — Vista principal de referencia

Misma cámara que la escena del archivo .skp (generada desde la geometría del modelo).

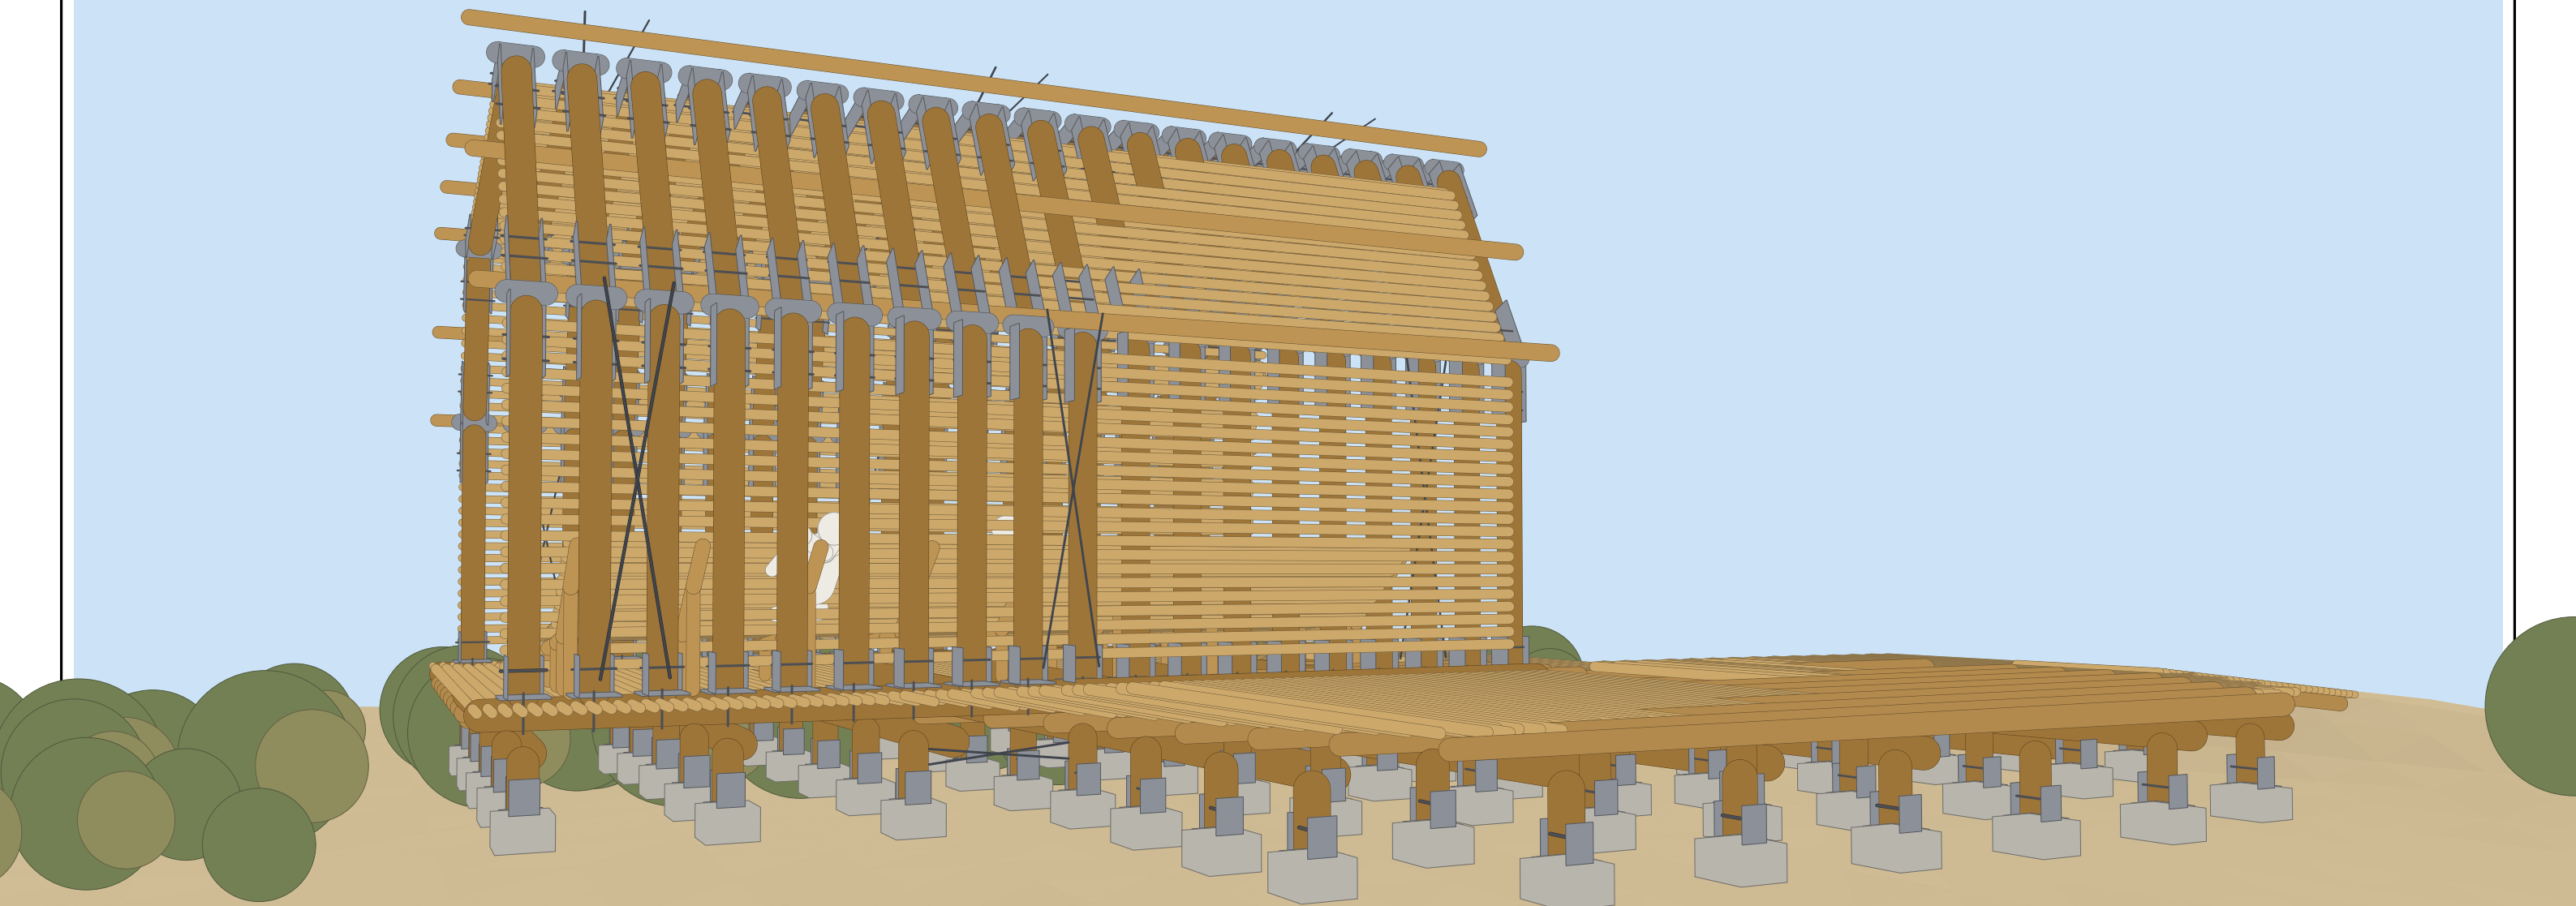


Escena 02 — Vista frontal: sección constante

Misma cámara que la escena del archivo .skp (generada desde la geometría del modelo).



Planta general (se omite el revestimiento de cubierta para leer pórticos y mobiliario)


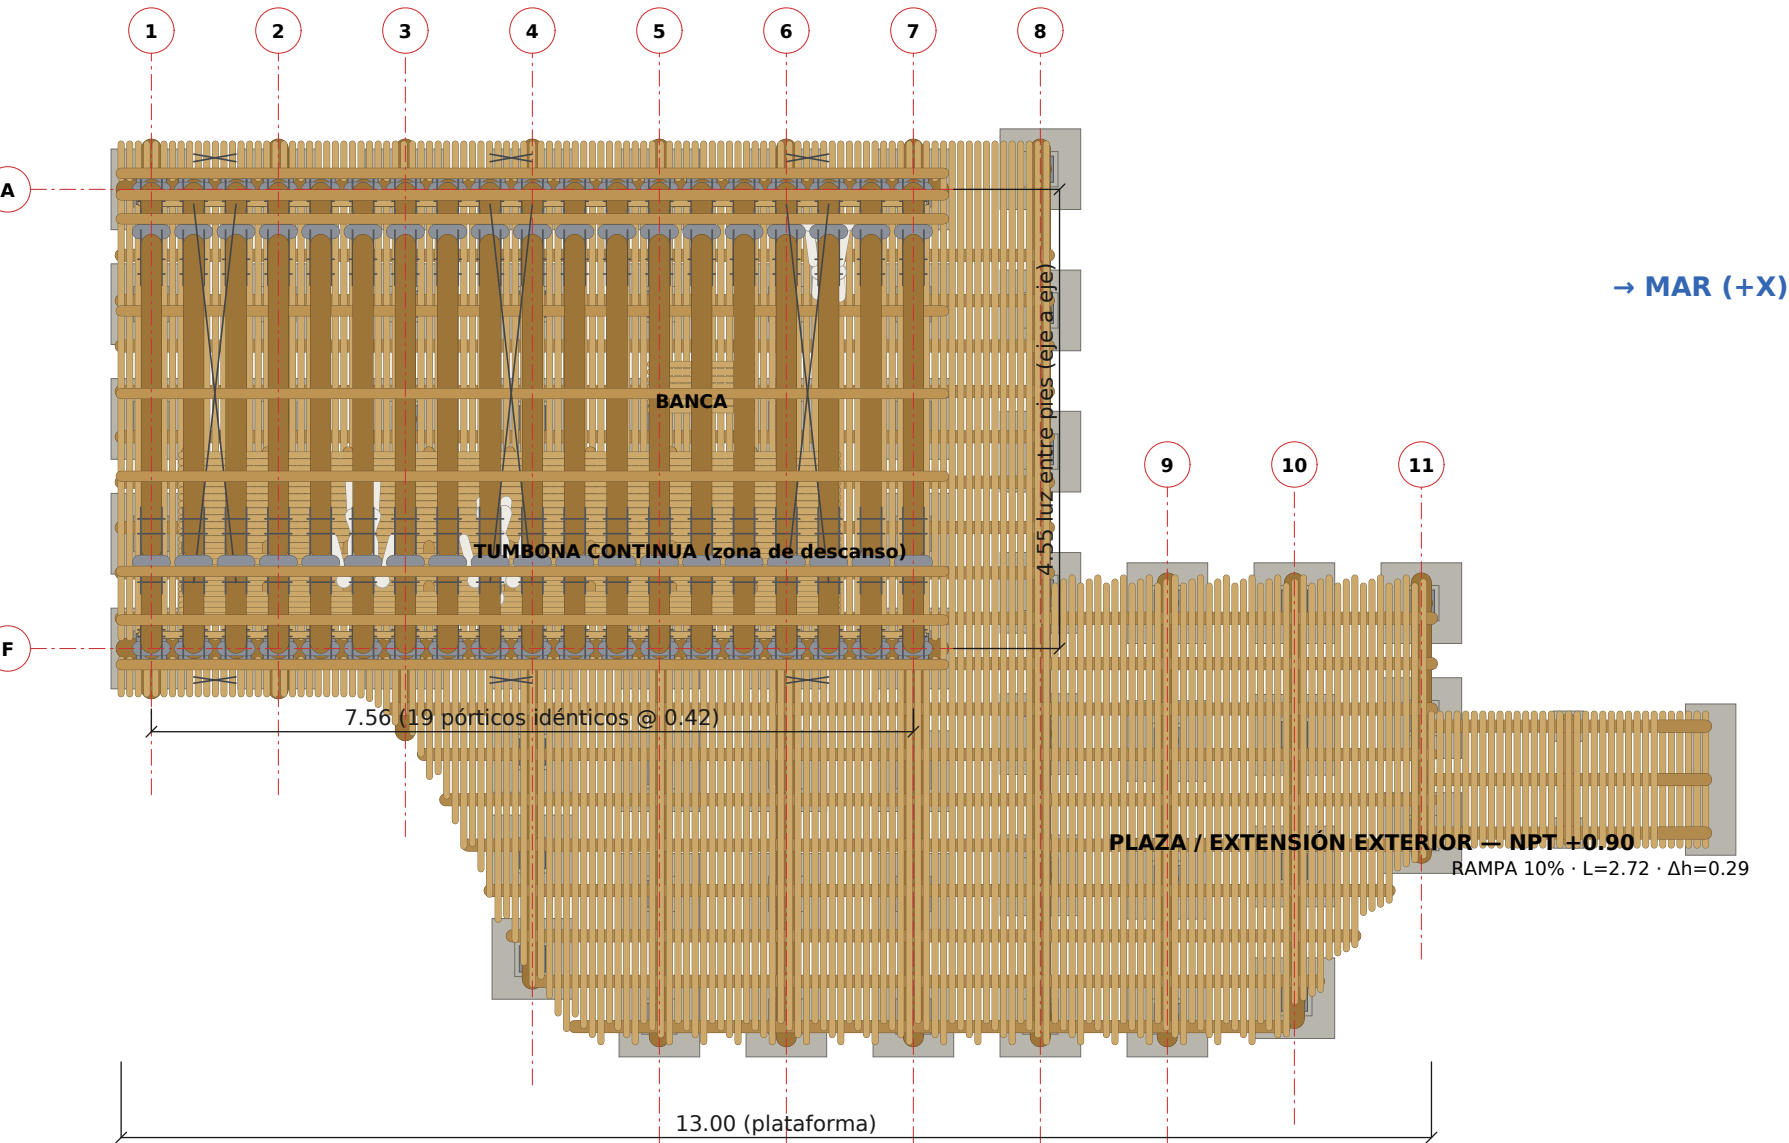


REFUGIO COSTERO DE CAÑA — PROPUESTA CONSTRUCTIVA V02

Planta general: huella de plataforma, pórticos, asientos, apoyos y cotas

Escala: 1:75 (A3) · Unidades: metros · NPT +0.90 (datum ±0.00)

Nivel 2: propuesta preliminar. NO apta para construcción sin cálculo estructural, estudio de suelos (E.050) y revisión de profesional colegiado.

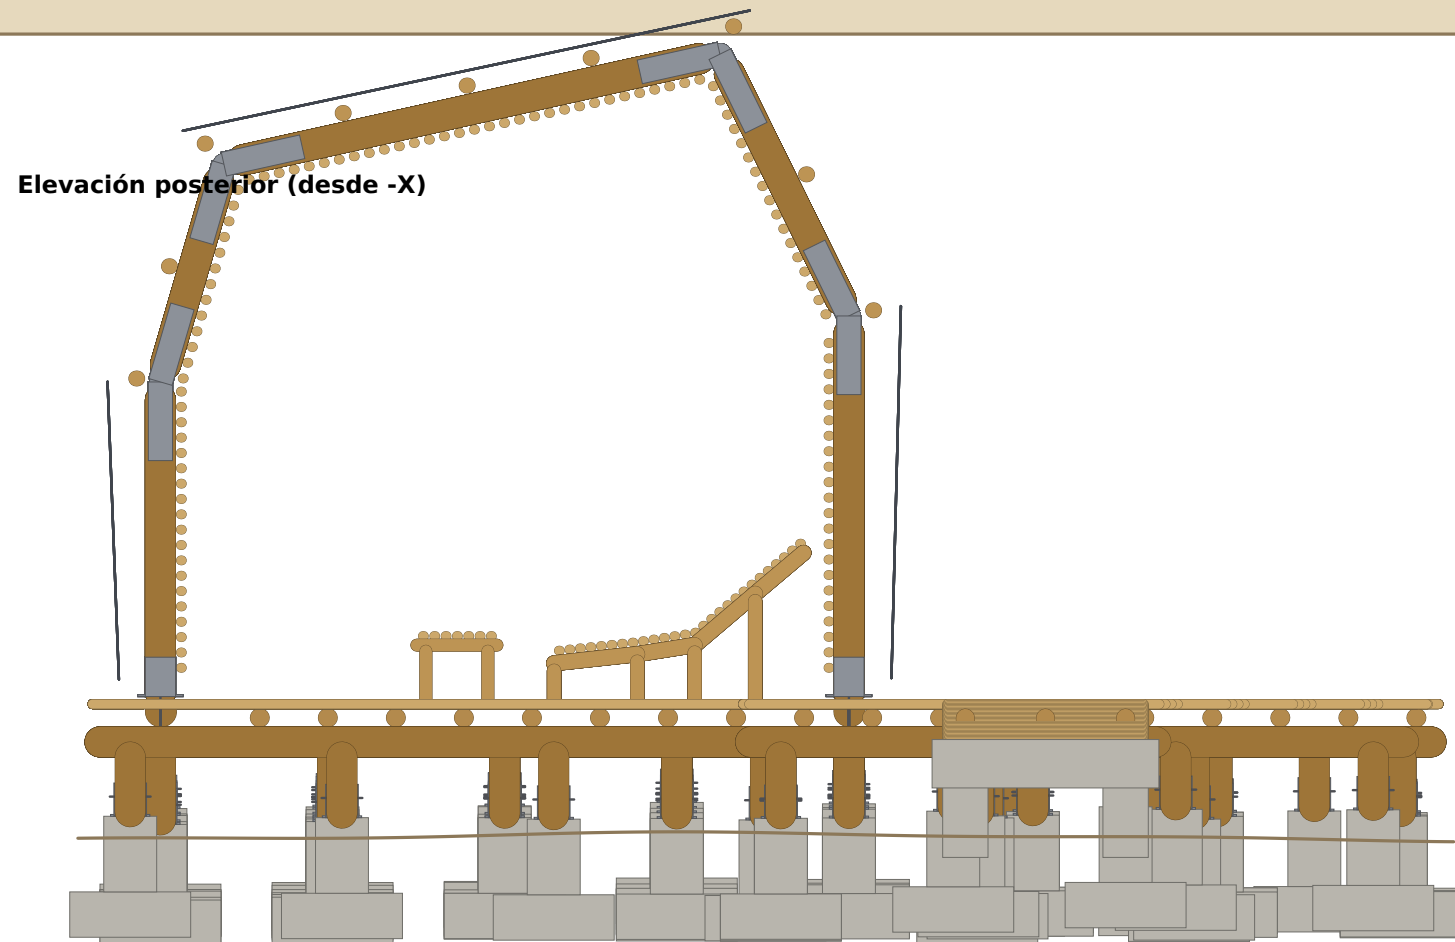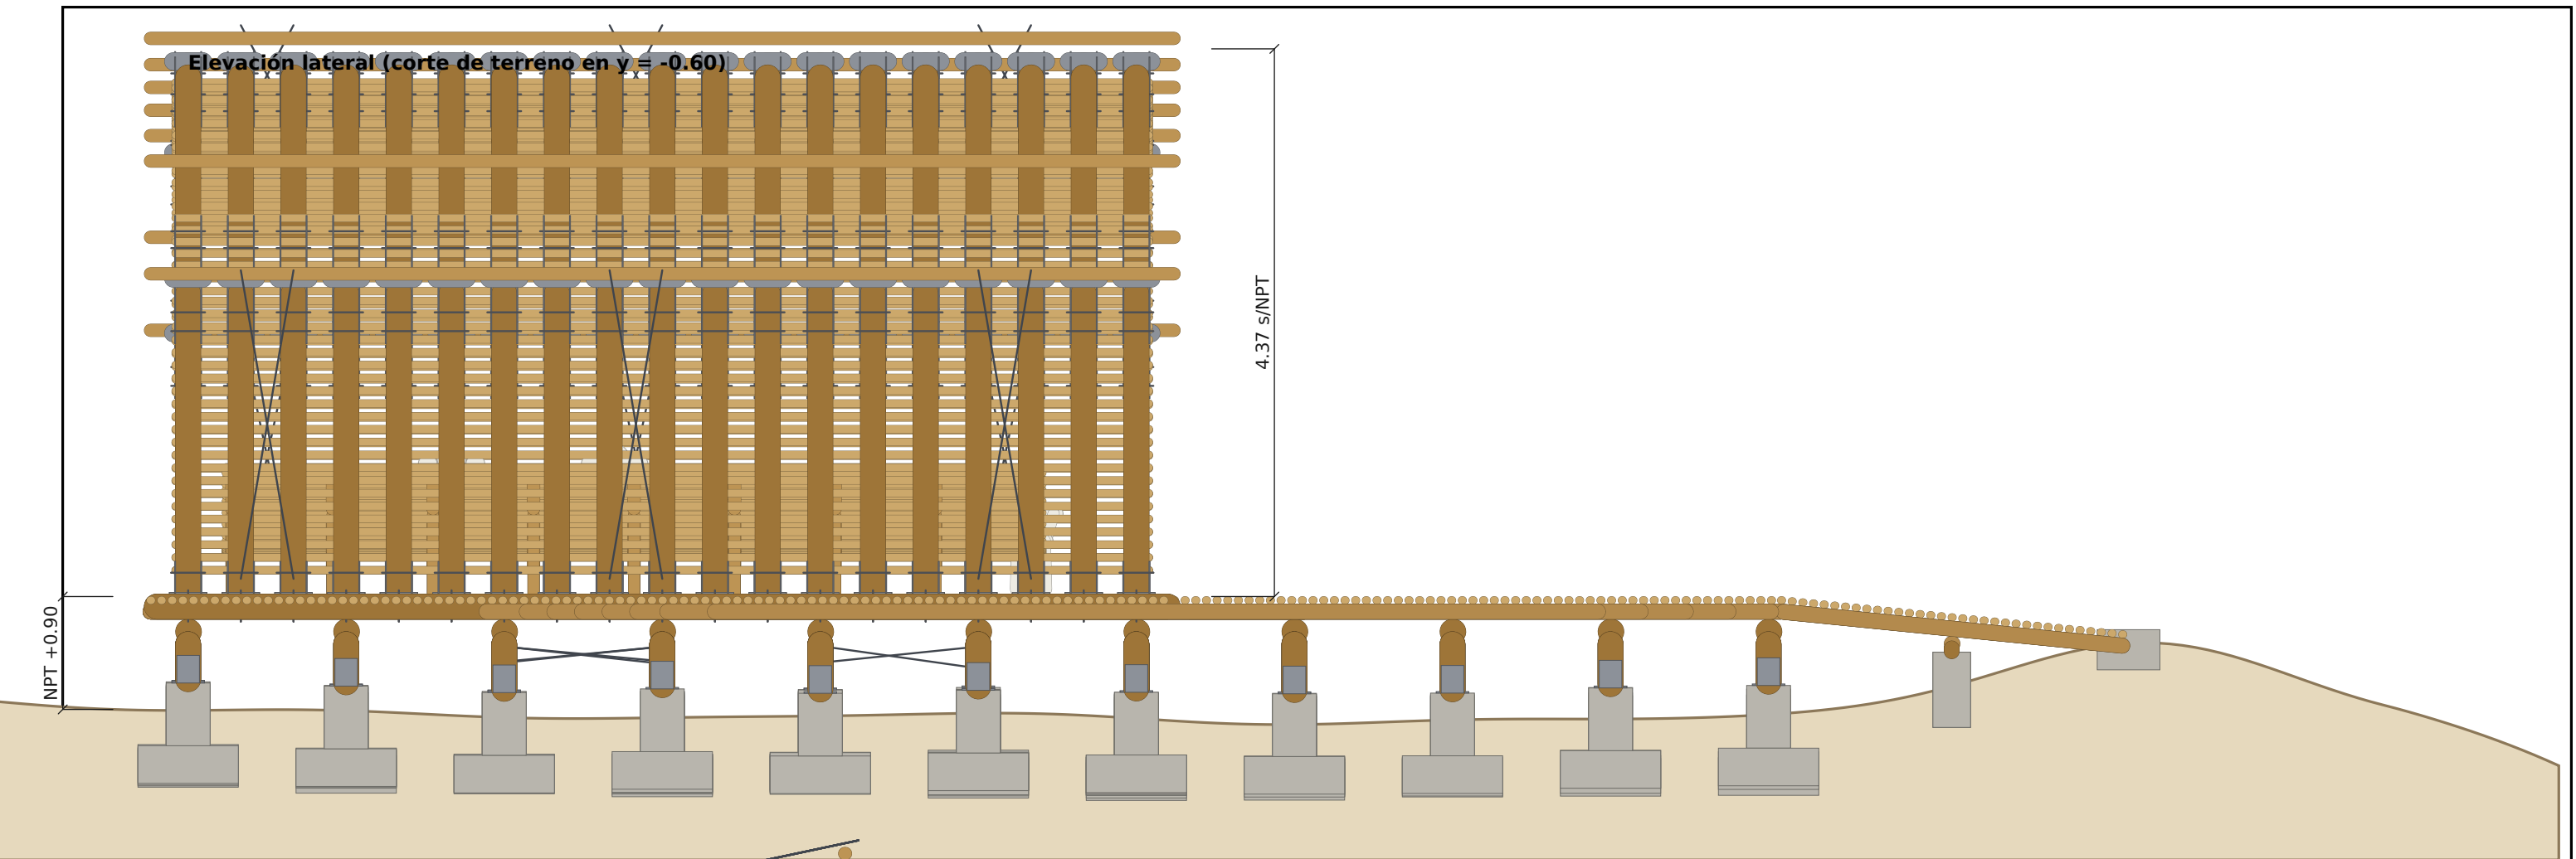

L-03

REFUGIO COSTERO DE CAÑA — PROPUESTA CONSTRUCTIVA V02

Elevación lateral (desde el lado 155°, -Y) y elevación posterior (desde -X)


Escala: 1:50 (A3) · Unidades: metros · NPT +0.90 (datum ± 0.00)

Nivel 2: propuesta preliminar. NO apta para construcción sin cálculo estructural, estudio de suelos (E.050) y revisión de profesional colegiado.

Sección tipo — longitudes de eje (m)

A-B (vertical)	2.050
B-C	1.500
C-D	3.360
D-E	1.930
E-F (vertical)	2.486
A-F (luz)	4.554

Rumbos de eje: 90.00°, 73.75°, 12.50°, -63.75°, -90.00°, -90.00°
Vista desde la boca hacia el fondo: lado A (165°) a la DERECHA.

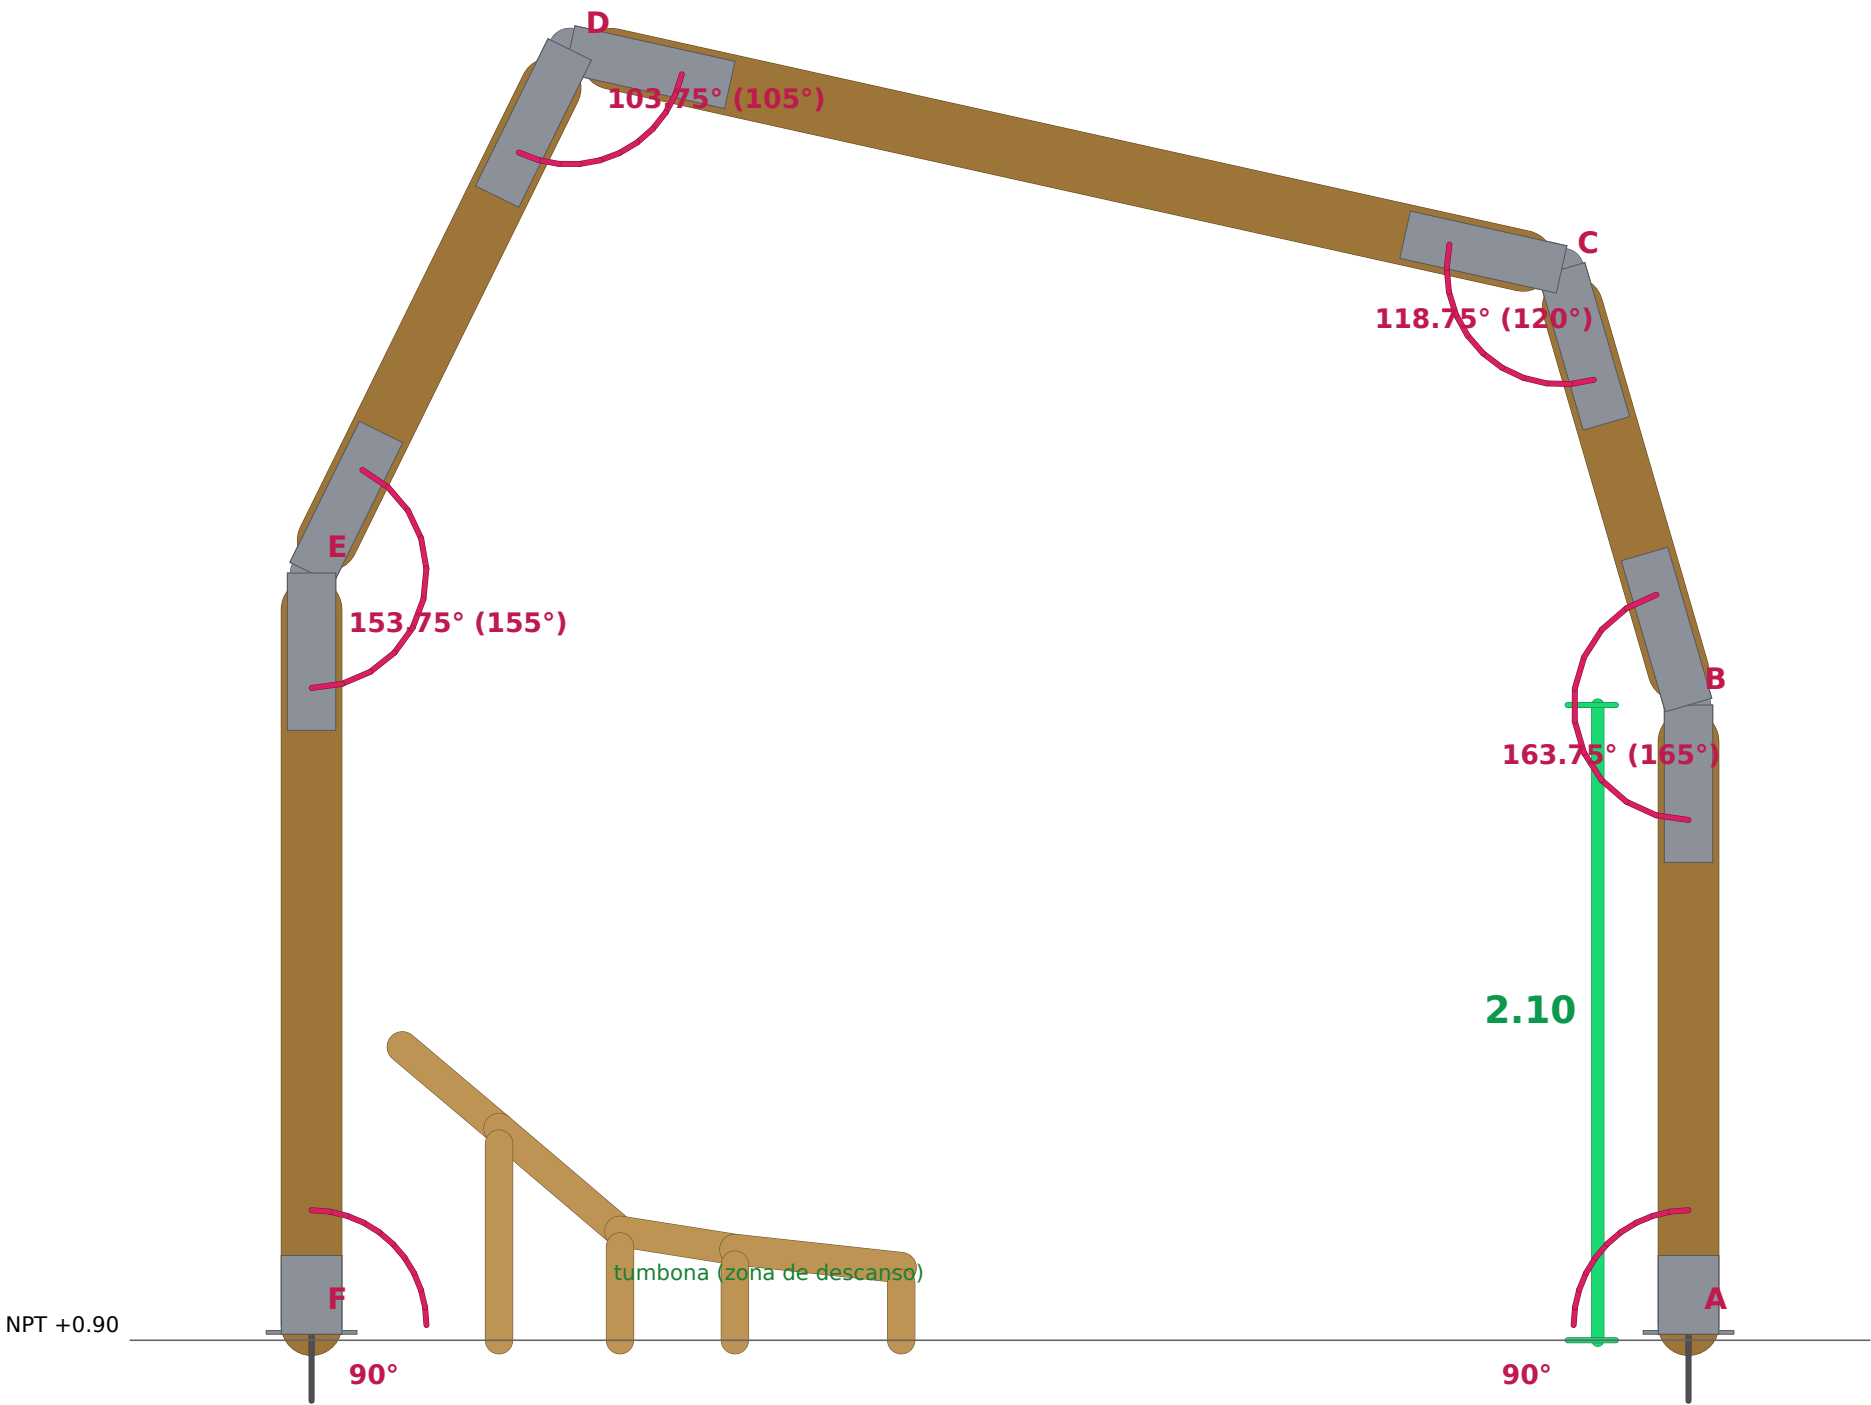

Pies A y F a 90° EXACTOS (verticales) en todo el largo: sección constante (extrusión recta).
Nominales 165/120/105/155 + 90 + 90 = 725° > 720°: se reparten 5° (1.25° c/u) en los quiebres.
Cota verde: NPT (+0.90) al quiebre de 165° del muro vertical A = 2.10 m.

L-04


REFUGIO COSTERO DE CAÑA — PROPUESTA CONSTRUCTIVA V02

Sección tipo (idéntica en los 19 pórticos), vista desde la boca: ángulos y cota 2.10 m


Escala: 1:25 (A3) · Unidades: metros · NPT +0.90 (datum ±0.00)

Nivel 2: propuesta preliminar. NO apta para construcción sin cálculo estructural, estudio de suelos (E.050) y revisión de profesional colegiado.

Planta de cimentación: 65 apoyos (zapatas aisladas + pedestales)

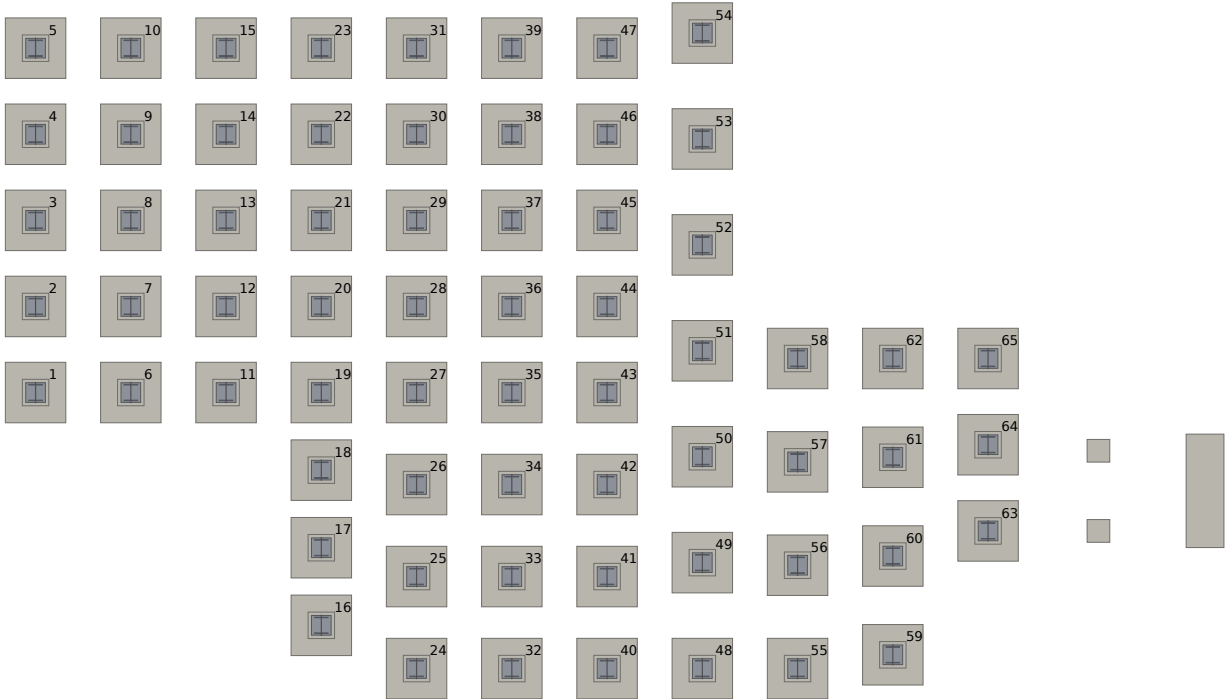


DETALLE 1 — APOYO TIPO (esquemático, sin escala exacta)

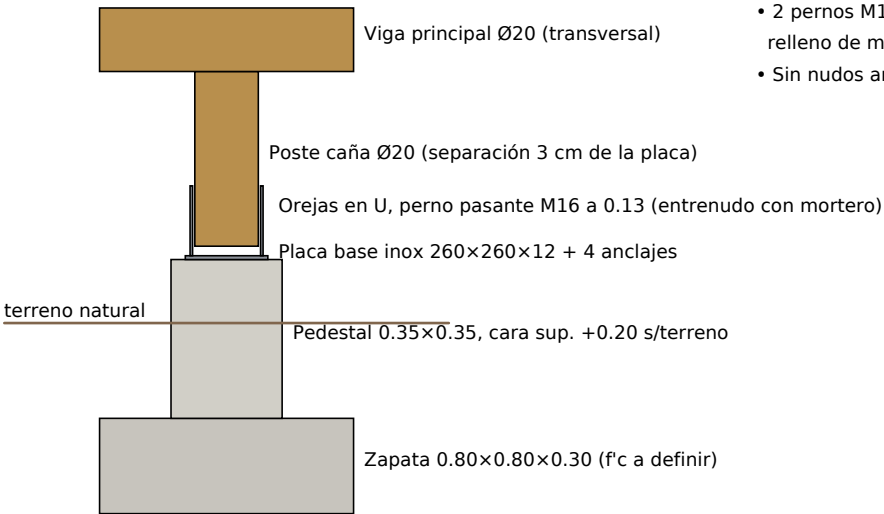

DETALLE 2 — NODO DE PÓRTICO (B, C, D, E)

- Corte de cada caña a $\geq (r+12 \text{ mm})/\text{sen}(\theta/2)$ del vértice para no interferir.
- Pletinas inox 8 mm a ambas caras + pasador central Ø14 (rigidez de nudo).
- 2 pernos M16 por extremo; 1.º perno a $\geq 150 \text{ mm}$ del corte, en entrenudo relleno de mortero (práctica E.100 / ISO 22156, a verificar por cálculo).
- Sin nudos articulados puros: el pórtico necesita nudo resistente a momento.

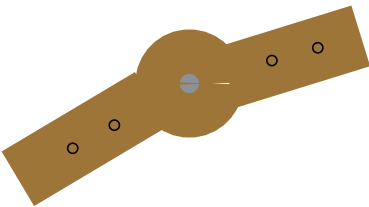

Hipótesis sin validar: suelo arenoso compacto, capacidad admisible a definir por EMS (E.050).
Zapata 0.80x0.80x0.30, fondo -0.60 bajo terreno; pedestal 0.35x0.35 hasta +0.20 sobre terreno.
Ninguna caña en contacto con el suelo. Anclaje en U inox AISI 316 + perno M16, entrenudo relleno de mortero. Separación mínima entre apoyos: 0.90 m.

L-05

REFUGIO COSTERO DE CAÑA — PROPUESTA CONSTRUCTIVA V02

Planta de cimentación y detalles preliminares de unión — PENDIENTE DE CÁLCULO

Escala: planta 1:100 · detalles 1:10 · Unidades: metros · NPT +0.90 (datum ±0.00)

Nivel 2: propuesta preliminar. NO apta para construcción sin cálculo estructural, estudio de suelos (E.050) y revisión de profesional colegiado.